


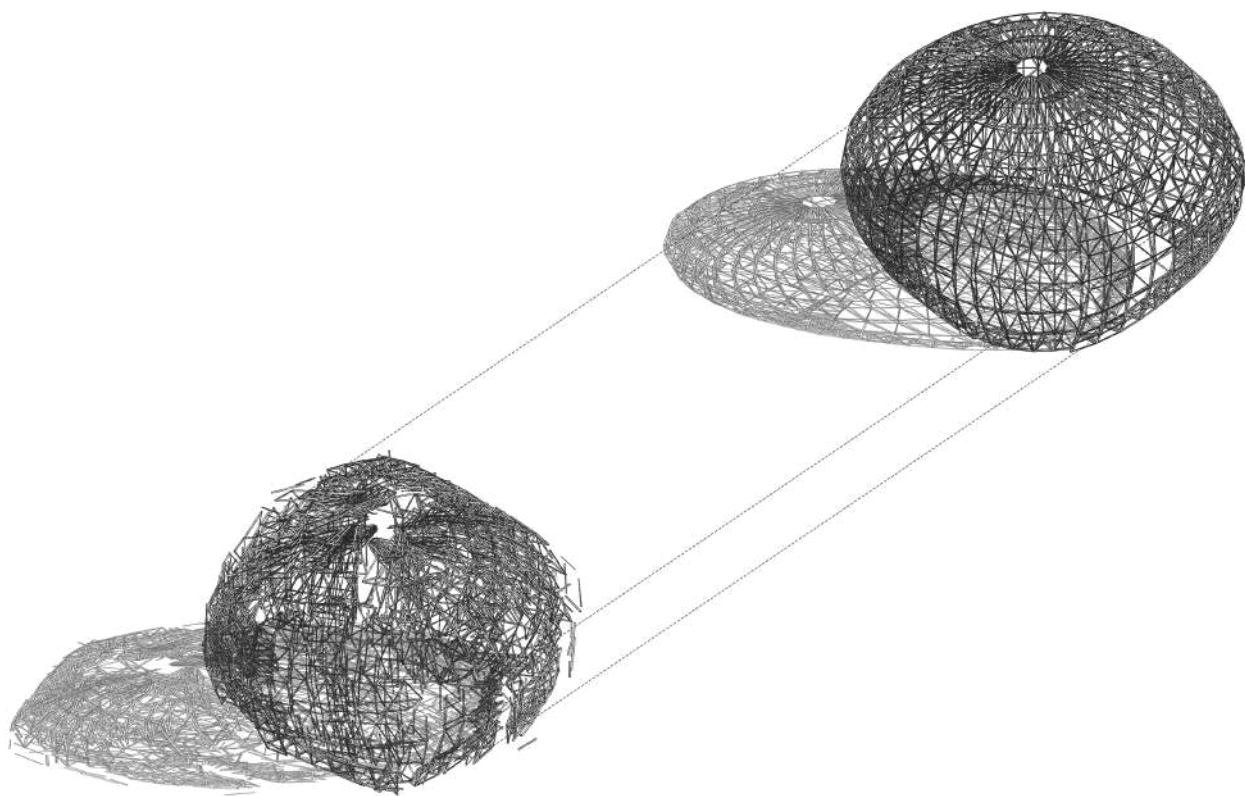

CRISTOBAL TORRES CID I ARQUITECTO

DATOS PERSONALES

+56987090331

crisbaltorrescid@gmail.com

torrescidstudio.myportfolio.com/work


@Torrescidstudio

Temuco, Chile



CONTENIDO

01- CASA DE ADORACIÓN BAHÁ'Í PARA TEMUCO	4-17
02- CENTRO DE CREACIÓN EN LABRANZA	16-21
03- CASA AGORA	22-31

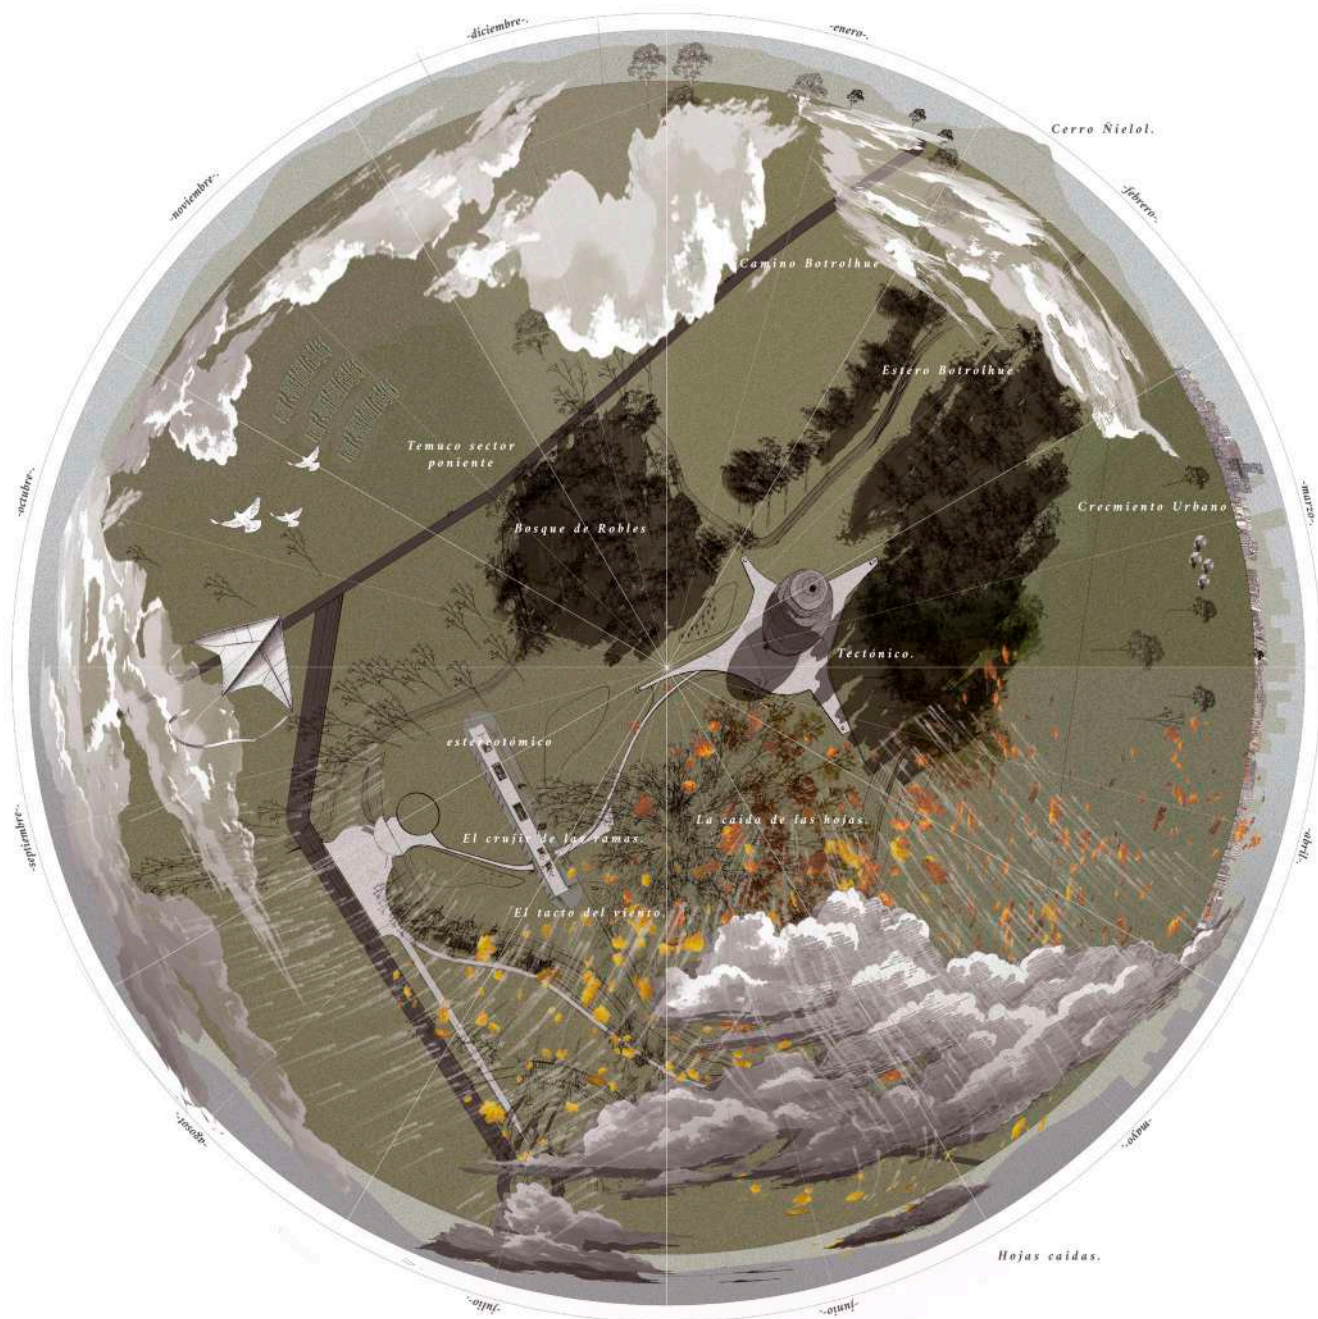

01

CASA DE ADORACIÓN BAHÁ'Í PARA TEMUCO

Proyecto de título


Año 2025

Guía: Carlos García

Una casa de adoración es un regalo, tanto como para las personas que lo usan para meditar, para orar, para hablar con su voz interior, como para el tiempo y el lugar en donde se posa, para preservar la naturaleza para generar un respiro entre una ciudad creciente.

Una Casa de Adoración Local Bahá'í para Temuco significa un reconocimiento de los históricos procesos sociales que ha llevado esta Fe en la región, así como también catalizar los esfuerzos planeados a futuro desde la administración Bahá'í para este territorio. Nace como respuesta a las palabras del Fundador de esta creencia (Bahá'u'lláh), quien decía que **en todos los lugares del mundo, en el futuro, habría Casas de Adoración donde todos sin importar sus creencias serían bienvenidos.**

Estos edificios responden al lugar y a la época en su tecnología. Se utiliza la madera con distintos fines, tanto en el interior como en el exterior. En paralelo, se diseña un edificio de recepción que asume la carga administrativa y logística del terreno.

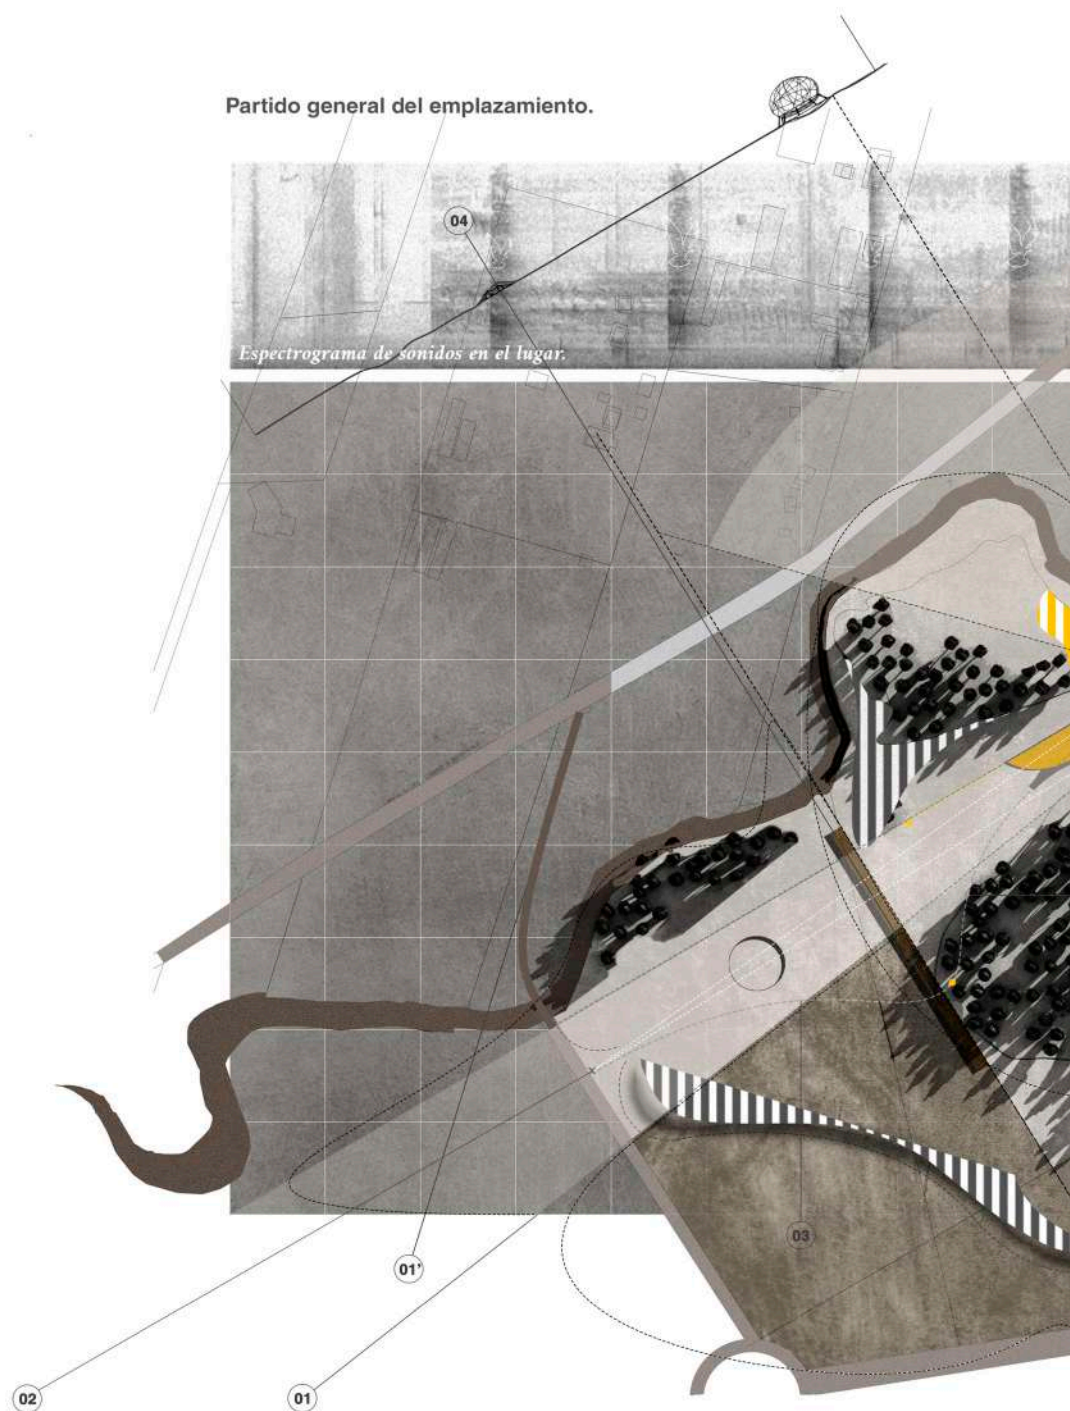

Estratos de lo sagrado

Si tan solo recordaras...


Como si dejáramos caer una semilla para el espíritu en el borde de la creciente ciudad de Temuco, Chile. En un punto estratégico para que, cuando el crecimiento de la ciudad se derrame a mayor radio, este sitio se ofrezca como respiro, donde se inhala más lento.

A mayor sacralidad, mayor debe ser la preparación para el encuentro, nos recordaba Christopher Alexander. ¿Cómo acompañamos ese tiempo? El templo es una Casa de Adoración Bahá'í donde todas las creencias son bienvenidas a orar, meditar o pensar.

En su camino a él, se pisa una losa elevada que no interfiere con lo silvestre. El buscador debe primero cruzar el edificio de recepción (04), donde el ritmo cotidiano se separa del rito, para sumergirse al interior

del bosque nativo. Bajo el ramaje, dentro del ruido blanco, una fuente de agua permite mojar el rostro y presionar sus párpados, para hacerse consciente del crujido leve del bosque vivo. Como escribió Bachelard: "todo soñador solitario sabe que oye de otro modo cuando cierra los ojos".

En el tramo (06), cuando cesa todo ruido exterior y los pies han aprendido a pisar más lento, aparece el edificio frente al buscador. Su forma recuerda un nido: mientras más denso el ramaje, más refugio ofrece. Al entrar, la luz se transforma en un lujo que se filtra entre sus prendas y acompaña la quietud, pero una quietud llena de movimiento interior, para así recordar que ya habíamos estado ahí reunidos.

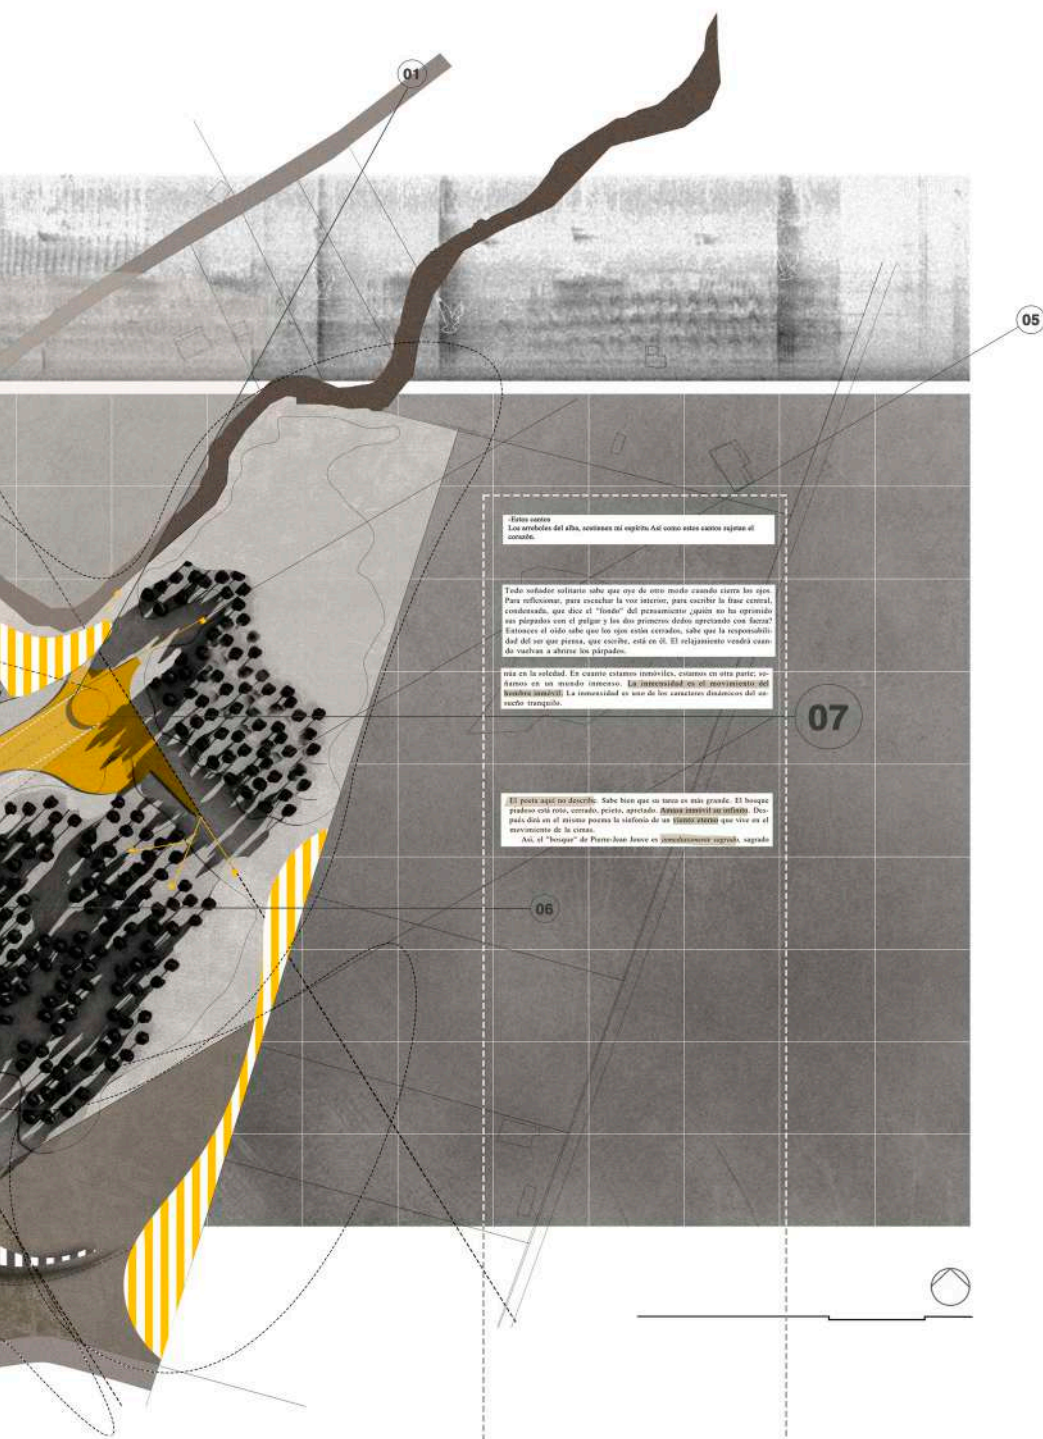

Como cuando
Los árboles del año, se ven en el espacio. Así como estos árboles se ven al
corazón.

Todo soñador soñador sabe que oye de otro modo cuando cierra los ojos.
Para reflexionar, para escuchar la voz interior, para escuchar la línea central,
condensada, que dice el "fondo" del pensamiento. ¿Quién no ha oprimido
sus párpados con el pulgar y los dos primeros dedos apretando con fuerza?
Entonces el cielo sabe que los que están cerrados, sabe que la respiración
del del se que piensa, que escribe, está en él. El relajamiento vendrá cuando
de vuelta a abrir los párpados.

vive en la soledad. En cuanto estamos inmóviles, estamos en otra parte; vi-
vemos en un mundo interior. **La intensidad es el movimiento del**
hombre interior. La intensidad es una de las sensaciones más profundas del es-
píritu humano.


El poeta aquí no describe. Sabe bien que su tarea es más grande. El poeta
puede estar vivo, cerrado, quieto, apretado. **Hay un interior en silencio.** De-
pués, está en el mismo punto la vida de un hombre interior que vive en el
movimiento de la vida.


Así, el "poeta" de Pierre-Jean Leves es **simultáneamente** **espíritu**, **seguido**

Un trascendente psicológico.

Las palabras escogidas al costado del
partido son lo que el mismo Gastón
Bachelard llama un trascendente
psicológico. En sus palabras: "El poeta
aquí no describe. Sabe bien que su
tarea es más grande". Estas citas son
también referencias e inspiraciones
utilizadas para pensar los espacios del
proyecto.



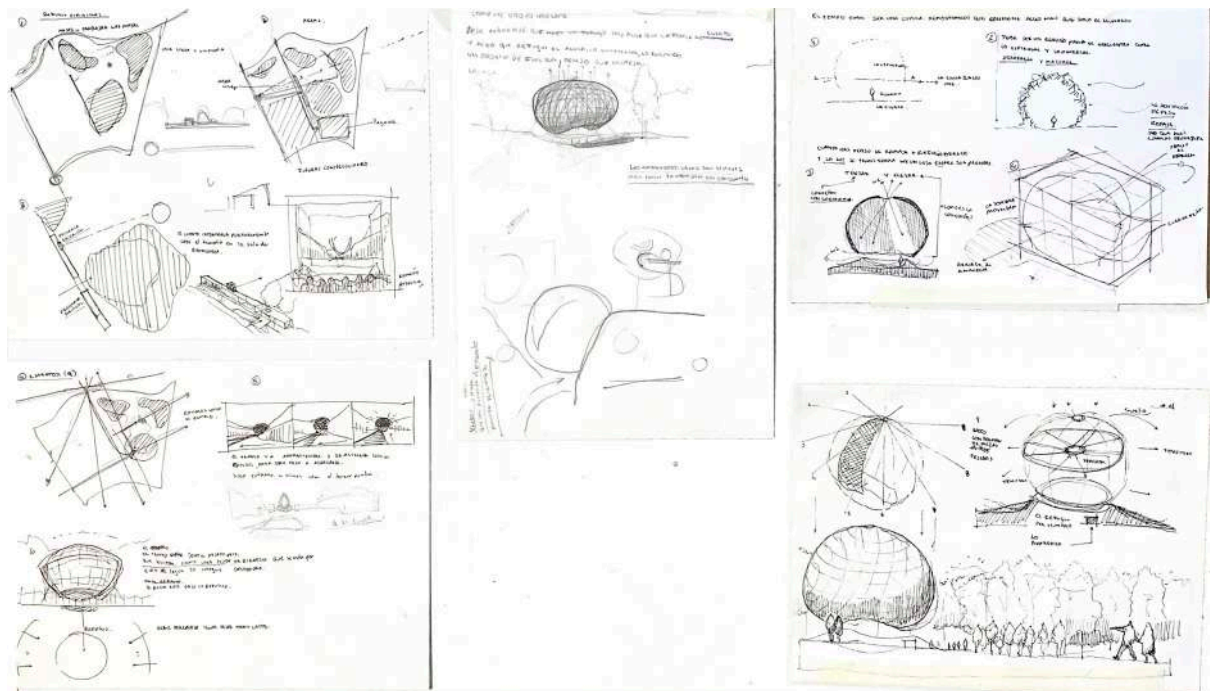

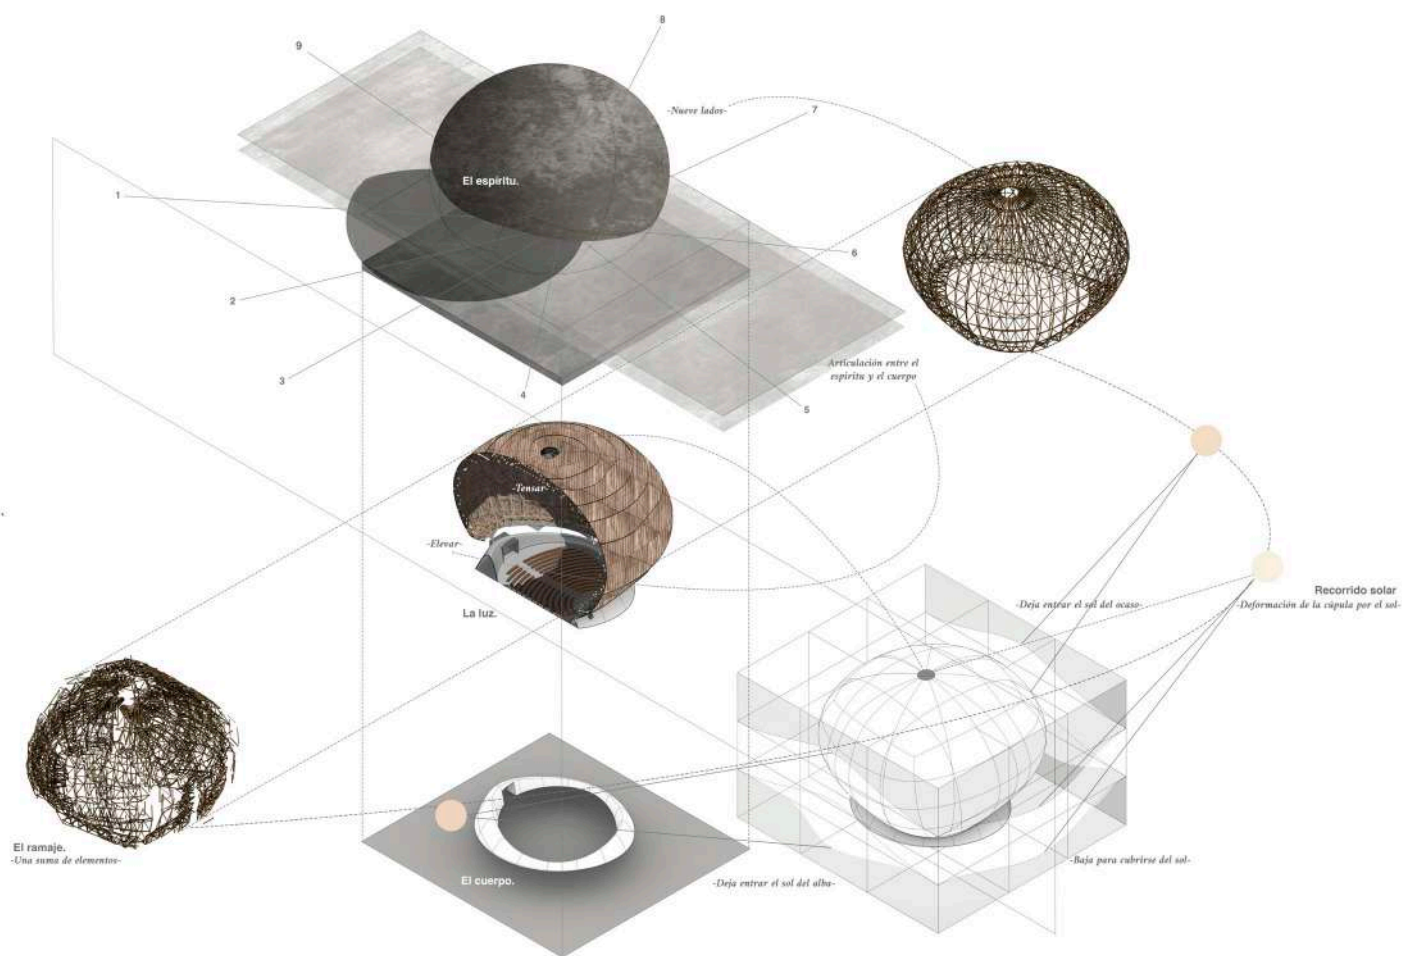


Como un nido

En el sur del continente en un meridiano alejado del calor constante durante el año la imagen ancestral de un refugio cambia. Es distinta contiene un ramaje que podría ser comparado con los nidos globulares, donde solo se abre en el acceso porque este es necesario.

Cuanto más denso es el ramaje, más refugio ofrece, y la luz se transforma en un lujo que se filtra entre las prendas que visten al edificio. Por ende, la luz solo se deja pasar de dos maneras: la primera, a través de un **óculo que tensa el espacio**; y la segunda, en el borde entre el ramaje y su soporte, elevando la estructura principal.



La cúpula se deforma, **permitiendo la entrada de la luz del alba**, protegiéndose del asoleamiento directo del mediodía y abriéndose al sol del ocaso.

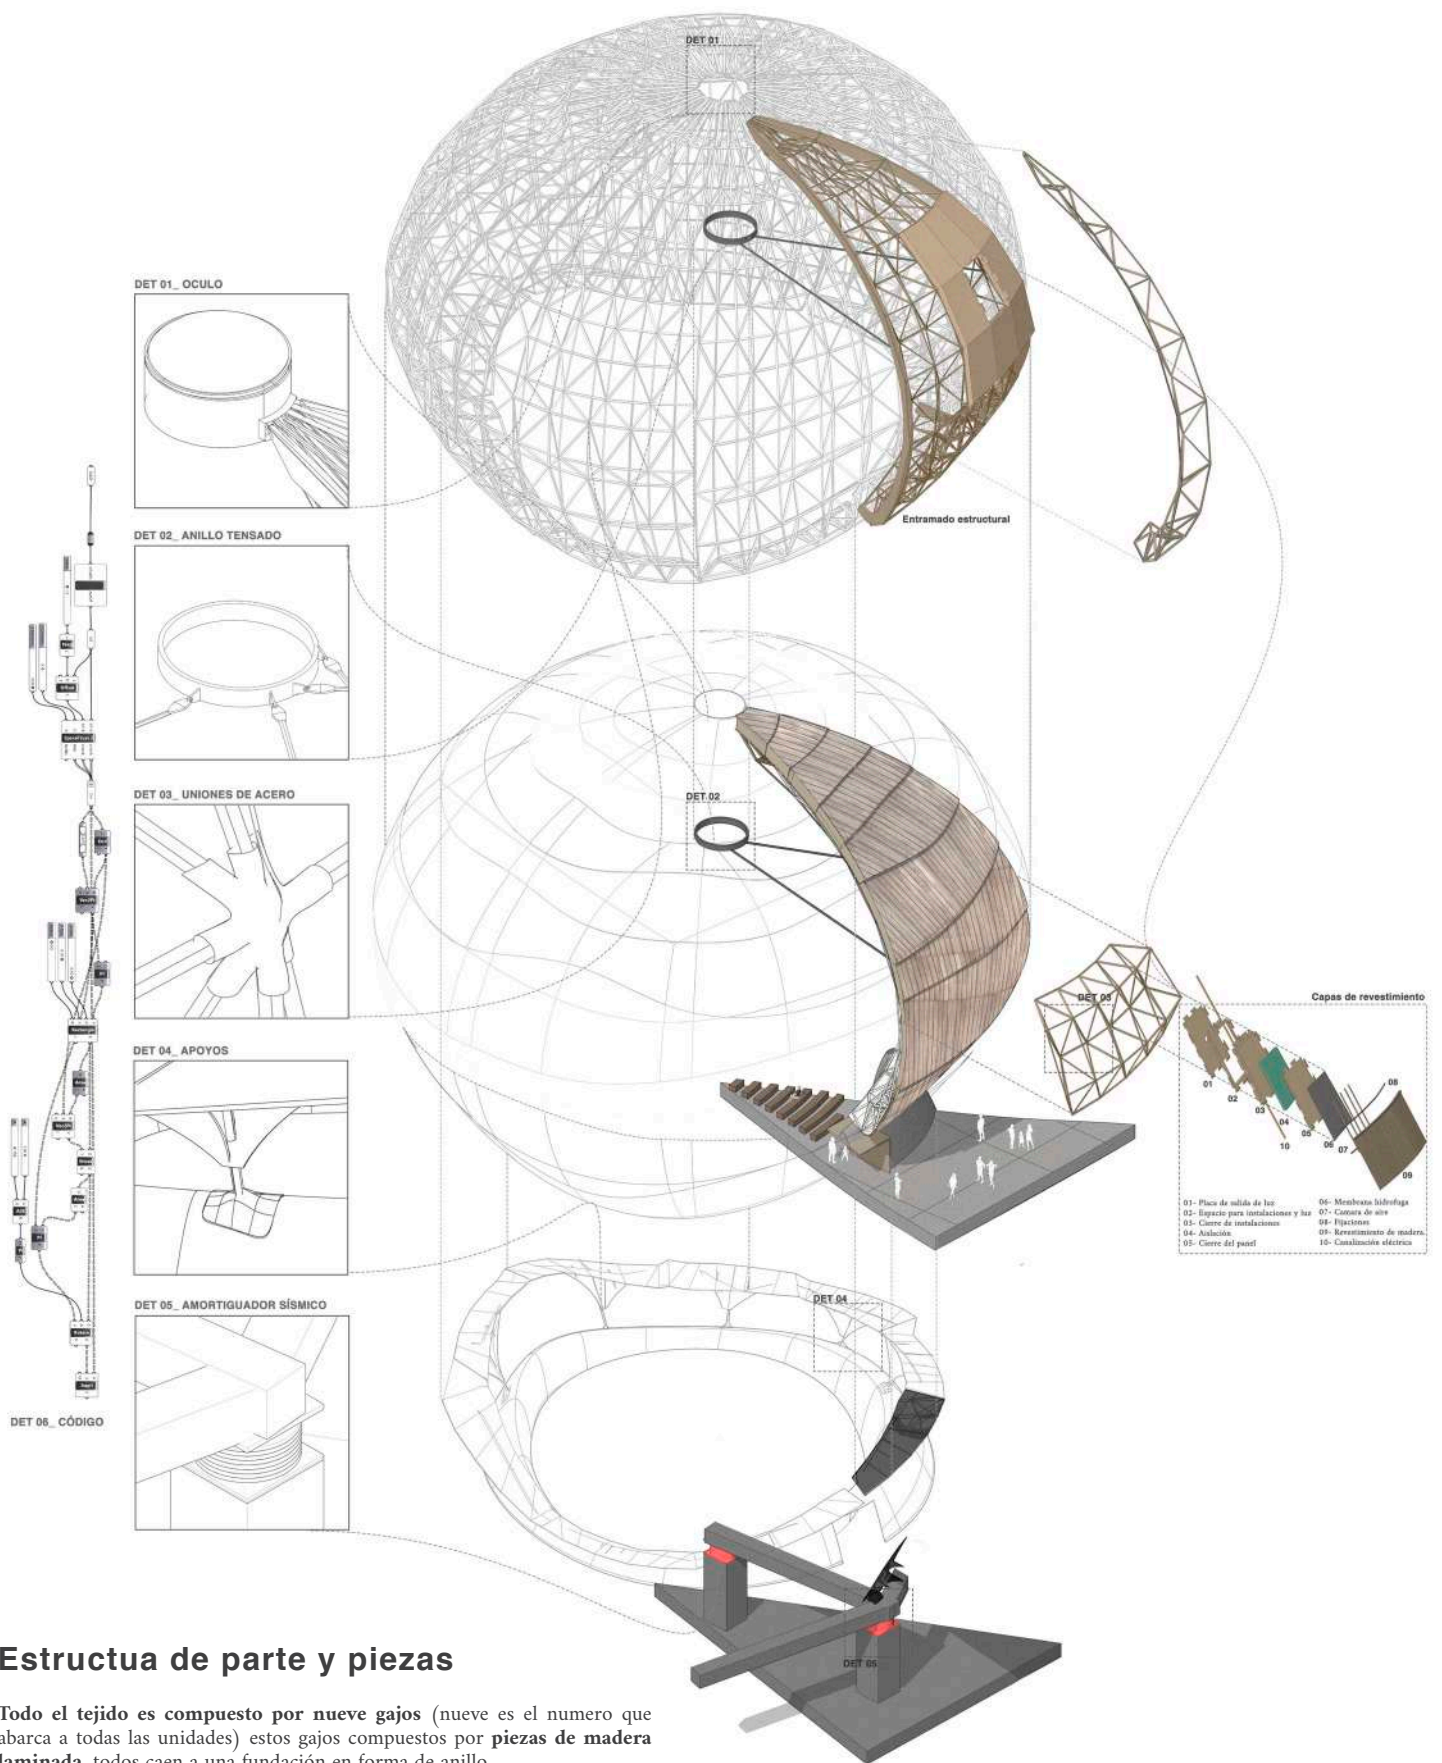



Estructura de parte y piezas

Todo el tejido es compuesto por nueve gajos (nueve es el numero que abarca a todas las unidades) estos gajos compuestos por **piezas de madera laminada**. todos caen a una fundación en forma de anillo.

El oculo amarra a todos los lados sin dejarlos caer, esto simboliza que sin el componente espiritual, **sin esa luz, todo se separaría** y el edificio no podría funcionar.

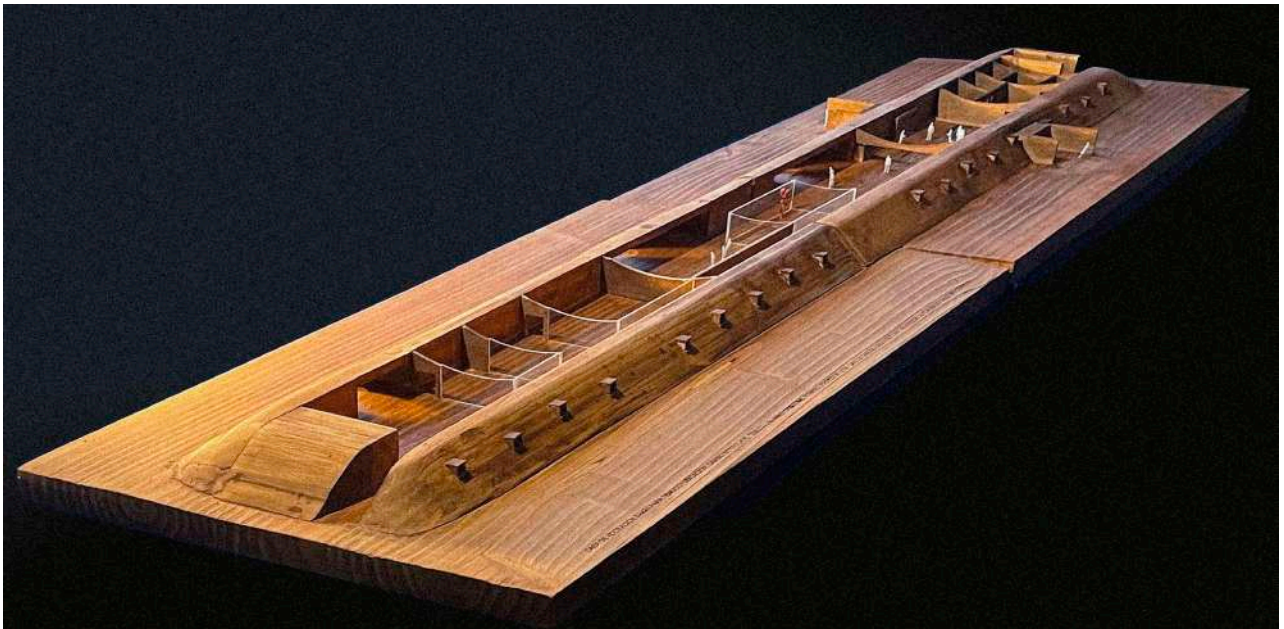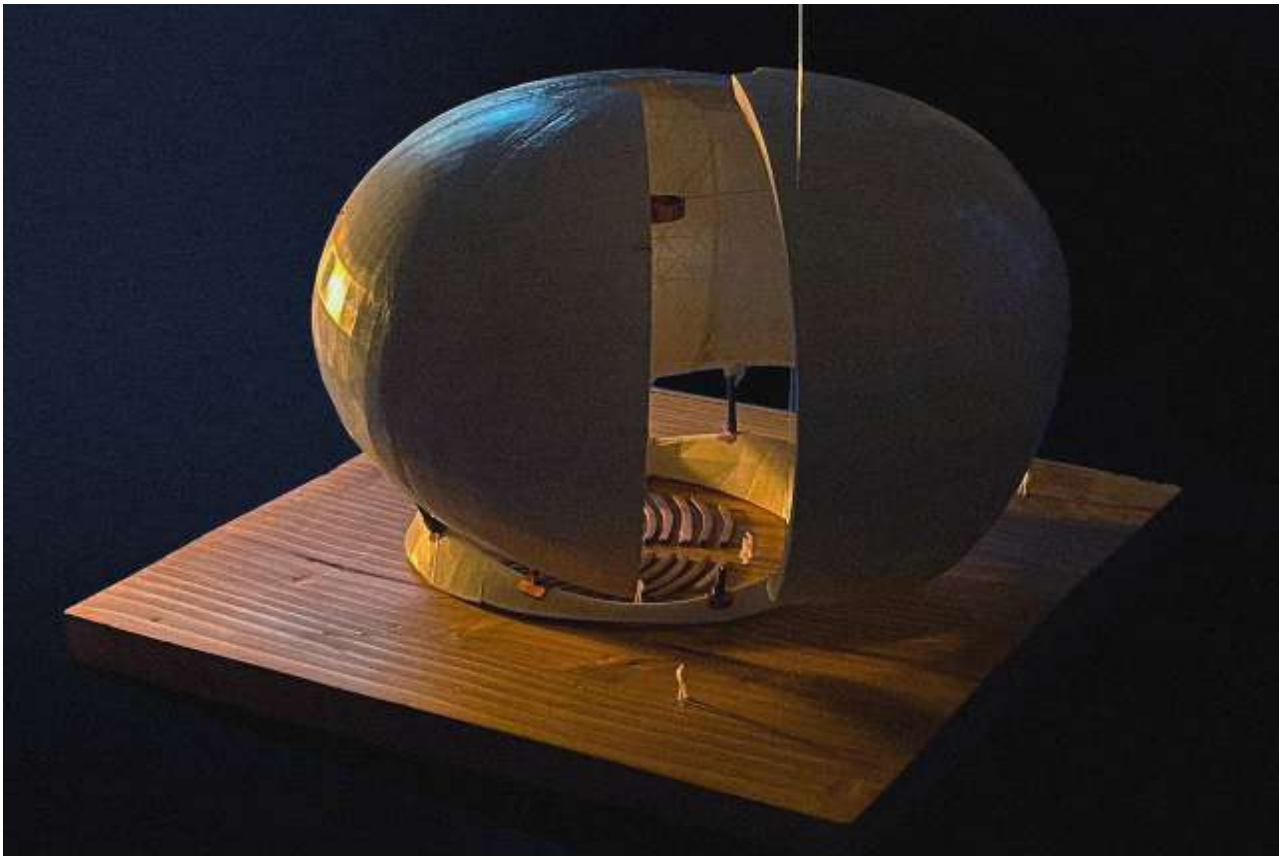

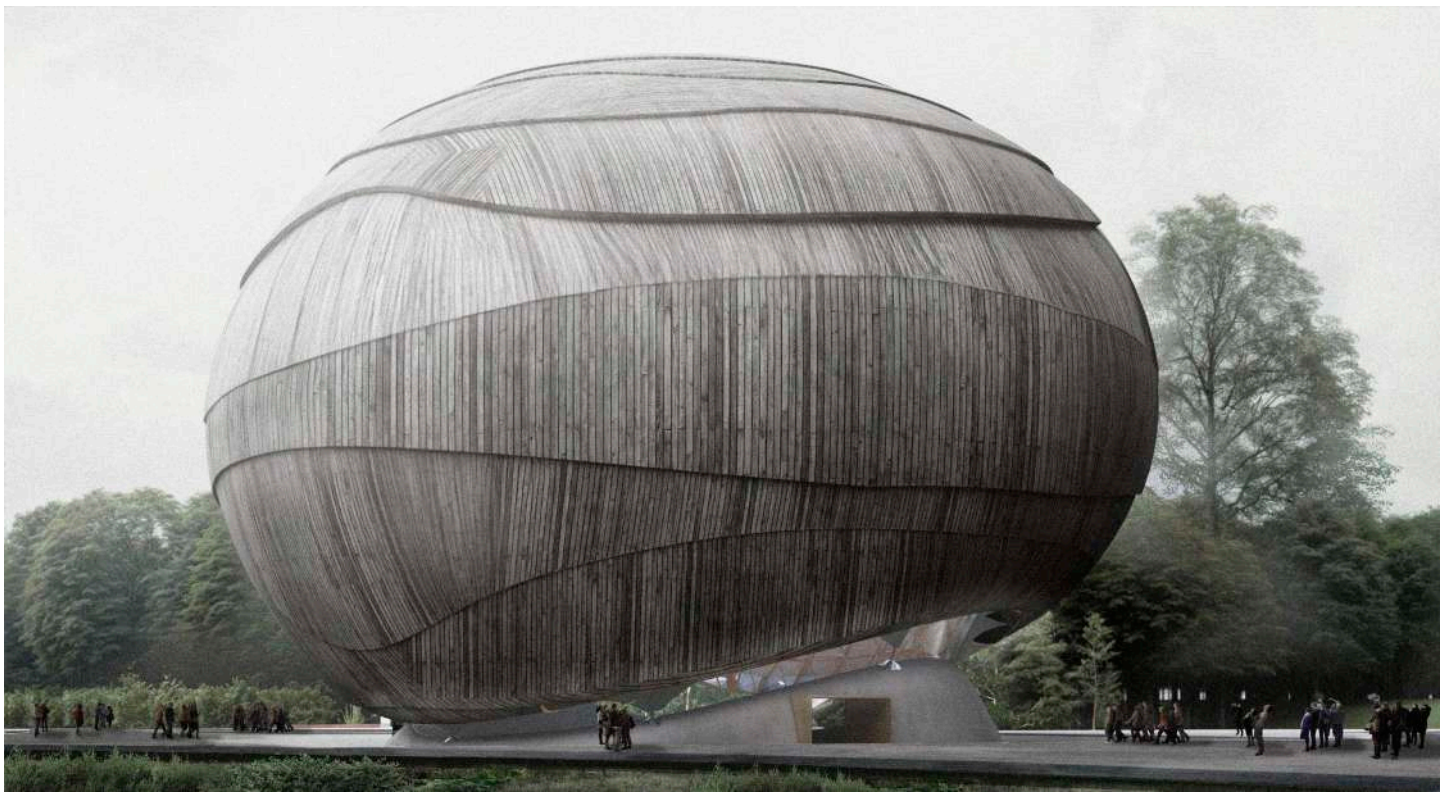

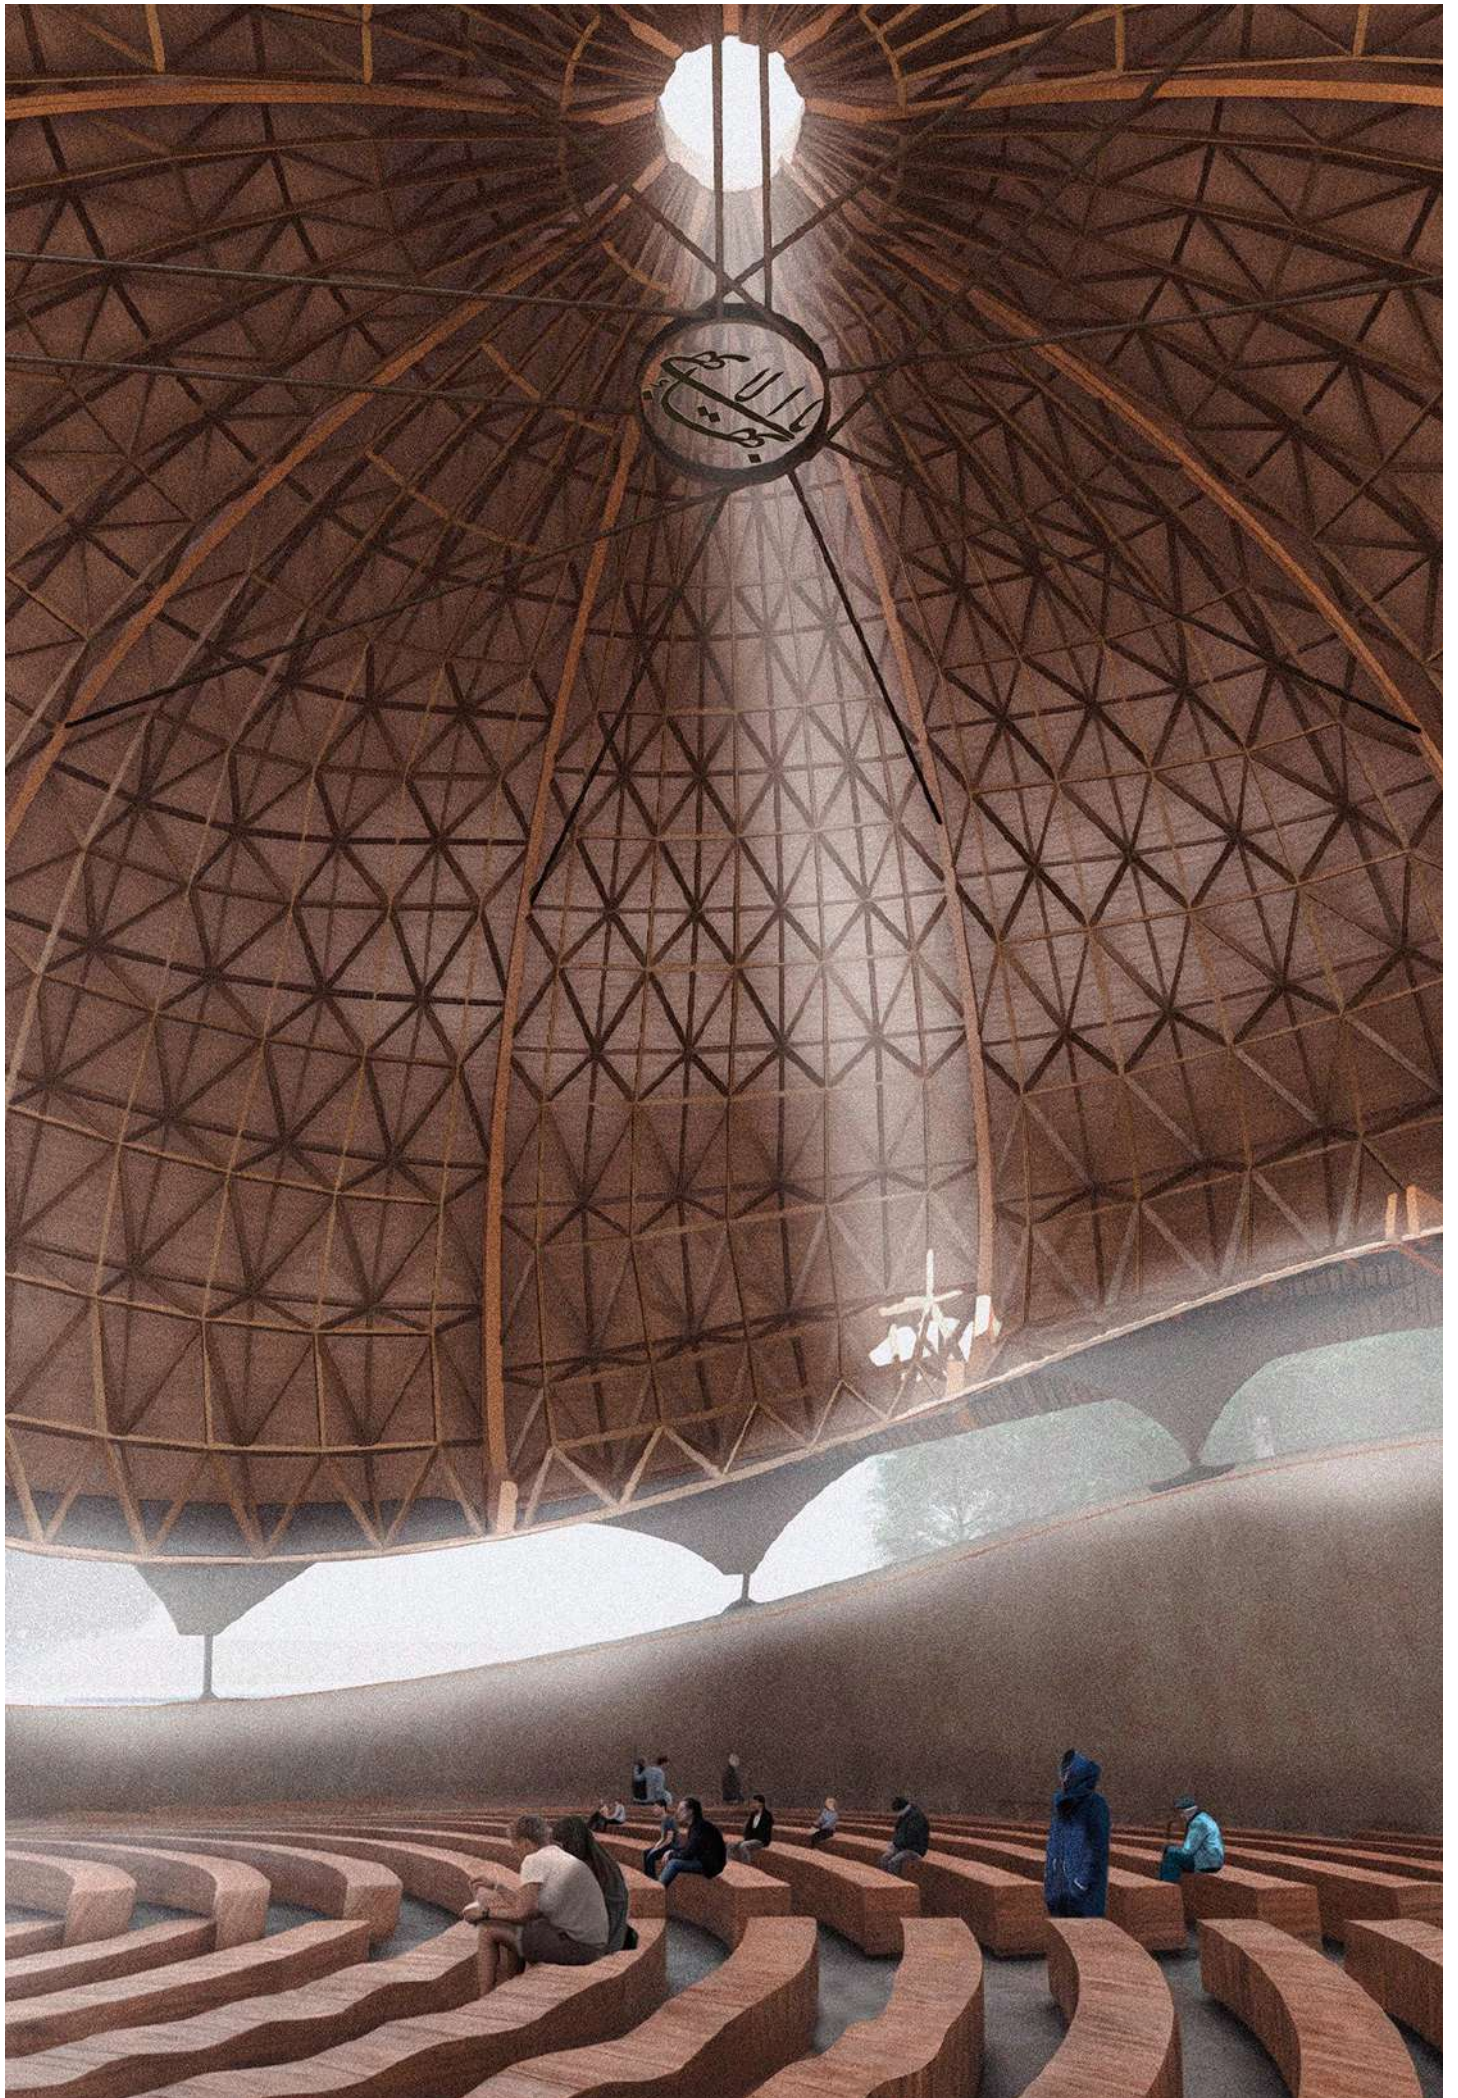



02

CENTRO DE CREACIÓN EN LABRANZA


Proyecto de semestre 9

Comenzamos con la pregunta: **¿cómo diseñar un espacio que incite a la creatividad?** El programa Cecrea busca impulsar un déficit detectado en la creatividad de los niños y jóvenes chilenos. A través de un espacio óptimo, talleres y tutores pueden desarrollar aquella creatividad inherente a la temprana edad. Los edificios Cecrea cuentan con variados talleres, que dan lugar a las artes plásticas, literarias, oficios y expresión corporal. El proyecto busca ser el lugar de encuentro común entre todas ellas: un espacio donde se encuentren, se observen e interactúen. Se ubica en el sector de Labranza, en Temuco, en un eje cívico que conecta directamente tres poblaciones jóvenes para dotarlo de masa crítica. Este sector está a la espera de una futura expansión, fortaleciendo su uso residencial. El terreno se emplaza en una esquina que actúa como nodo entre estas áreas.








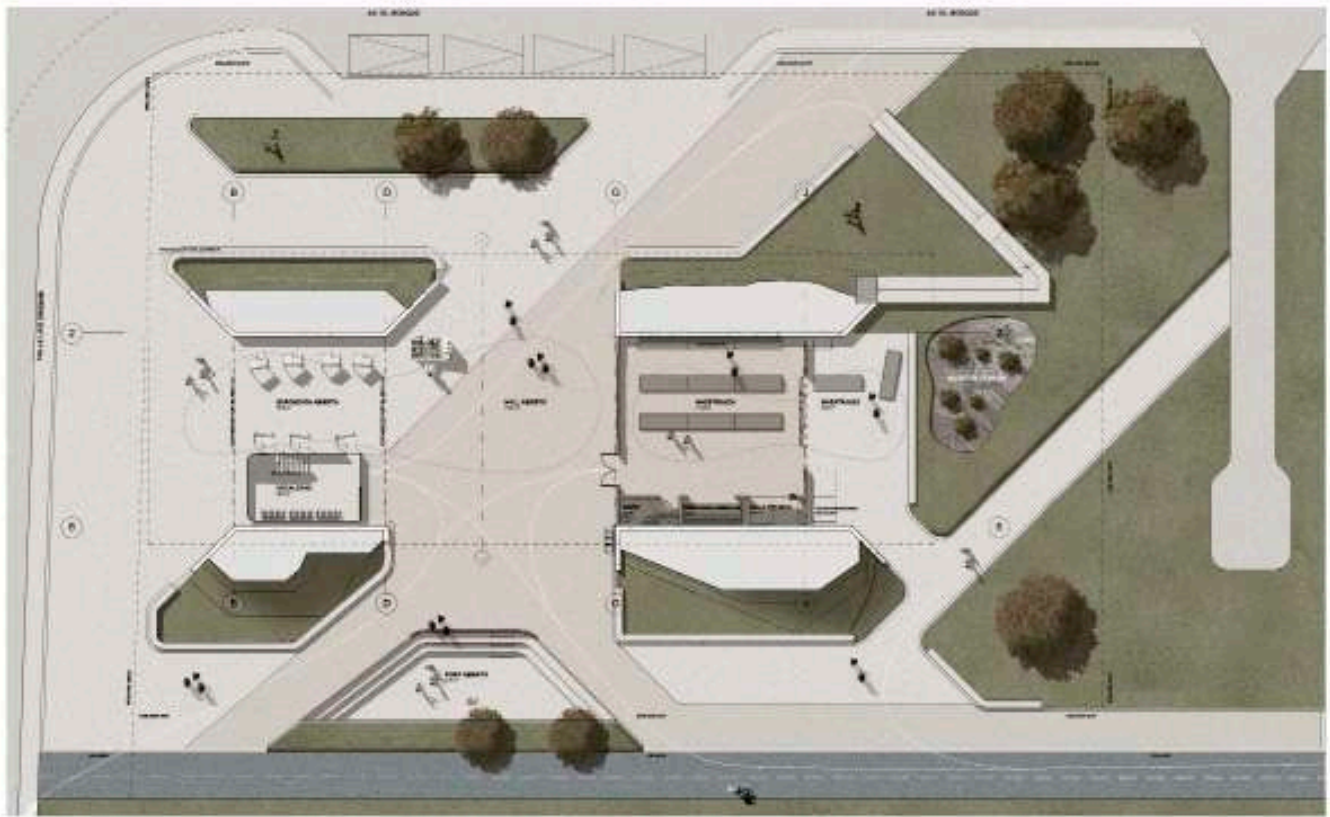


PRINCIPAL PLAN



SECOND LEVEL

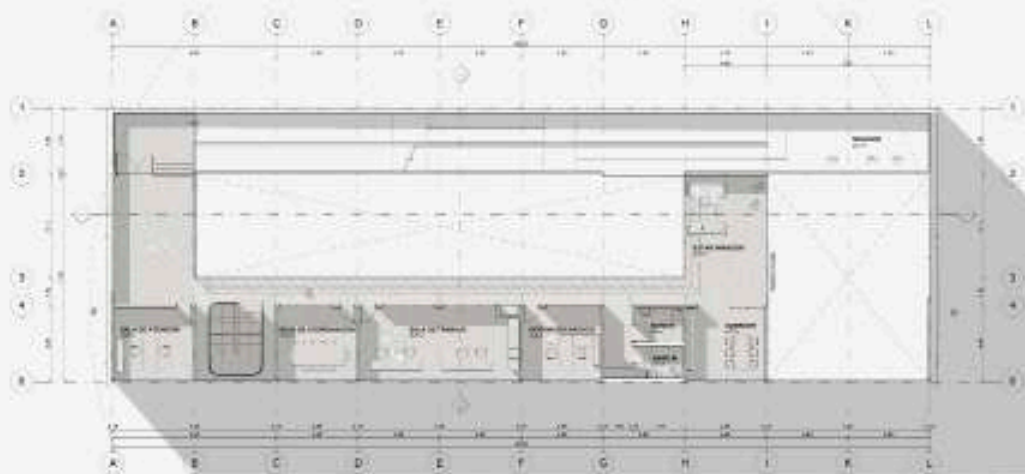

THIRD LEVEL

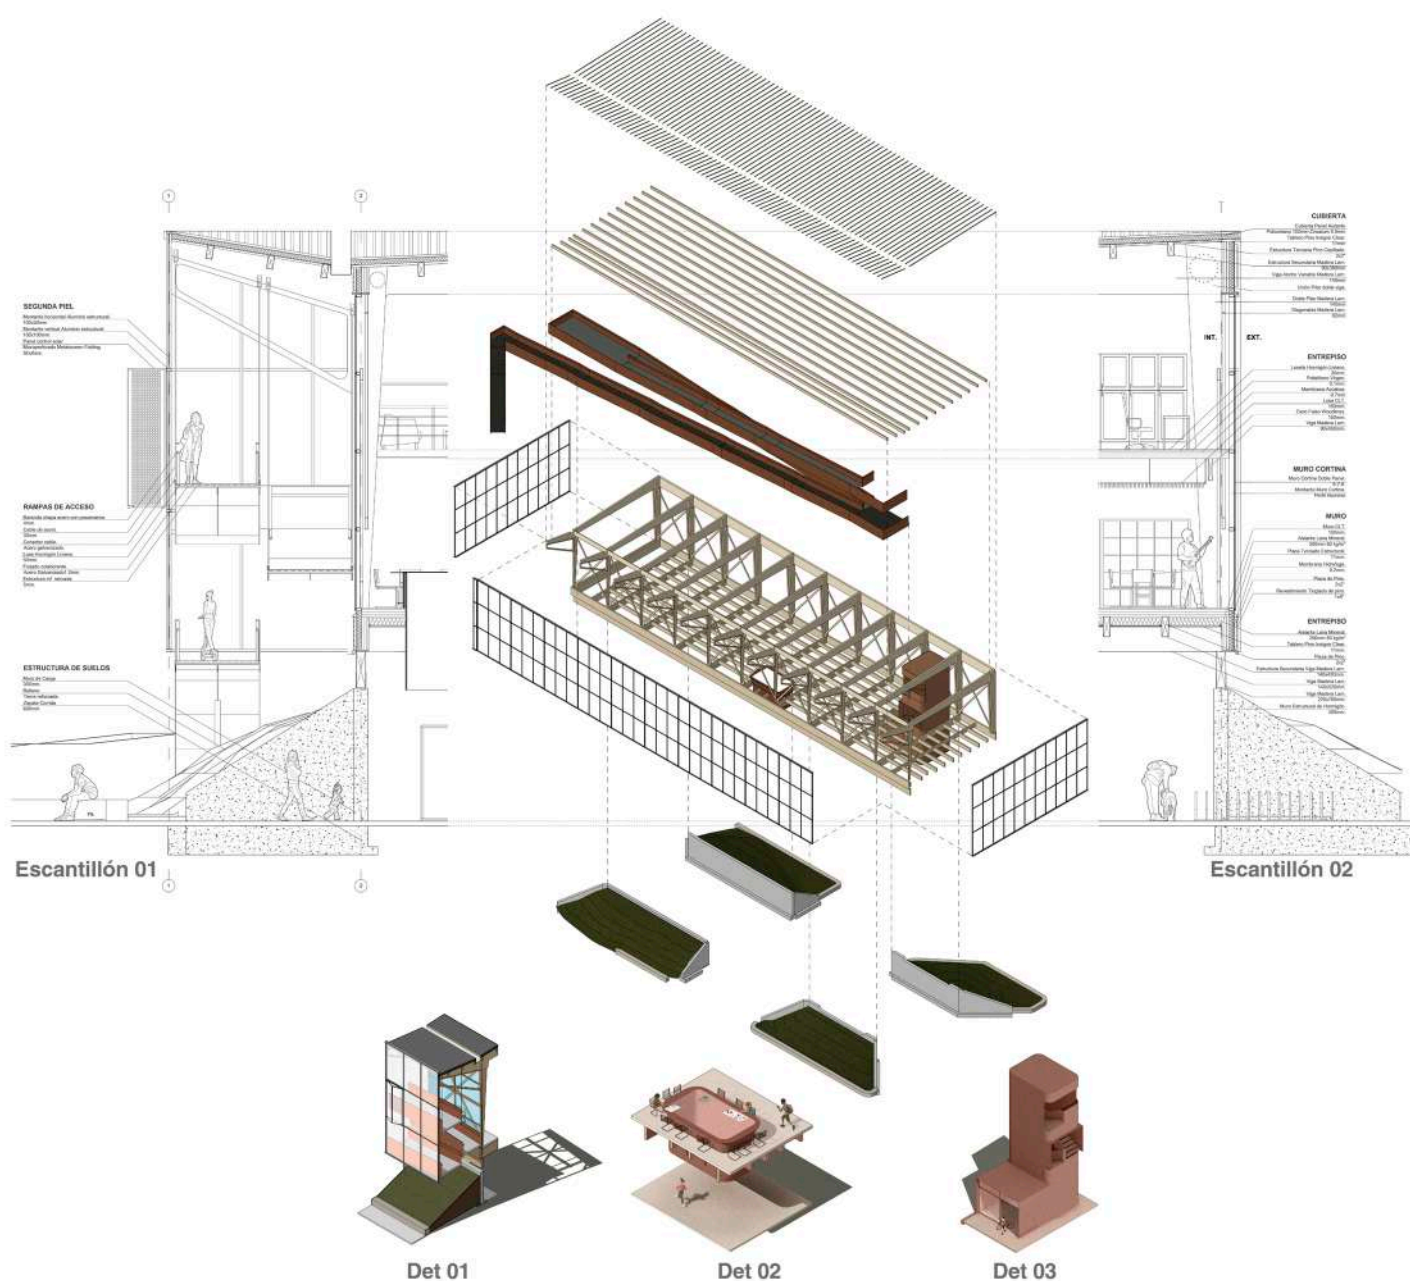

Detalles.

Desde los detalles constructivos hasta los espaciales, se plantea una búsqueda por aumentar las variables para quienes habitan el lugar: ver un mismo espacio desde distintas perspectivas, recorrer el edificio de múltiples maneras, o que una mesa funcione como una lucarna, son elementos que estimulan la creatividad.





03

CASA AGORA

Proyecto de semestre 7/ **Primer lugar Concurso Nacional Desafío NetZero2030**
Equipo 34 + Sebastián Maureira + Enzo Arriagada

El problema de la vivienda social en Chile es mucho más amplio que solo el desempeño energético. El diseño de la vivienda social debe **promover la cohesión social**, y hacerse cargo no solo de la vivienda, sino, que también del entorno en que ésta se emplaza y como éste construye ciudad. En Temuco, en la actualidad, principalmente el uso masivo de leña para calefaccionar genera el 90% de **la contaminación del aire**, esto ha alejado a las personas de los espacios públicos, desgarrando la cohesión social, y generando graves problemas de salud.

La casa Ágora es el resultado de un trabajo transdisciplinario que busca dar respuesta a esta problemática ambiental y social, al proponer **un conjunto de viviendas con elevados estándares de eficiencia energética**, acompañado por una **organización urbano-espacial que reconoce su contexto geográfico y climático, a la vez que promueve la cohesión social y las interacciones entre vecinos**, aquí resalta la importancia del patio central como articulador de la vida comunitaria al aire libre, integrando el equipamiento común, con el juego, el ocio, y como **respiro para los habitantes de cada conjunto**.

Por lo anterior **el proyecto es un ordenamiento capaz de amortiguar y atenuar las frecuencias de la ciudad que se vuelcan hacia el medio natural**. El gesto que ordena es un eje que recorre desde la ciudad, hasta coronar en el borde río, creando una huella de espacio público que se entreteje con vegetación nativa. En su interior se encuentran **conjuntos que como gesto, buscan despertar y abrazar la cohesión social vecinal extraviada**. Dejando en su interior áreas verdes y públicas, donde a través de huertos comunitarios, espacios recreativos, vegetación y sistemas de uso compartido, se fortalezca **el sentir de una actuar mancomunado**, dando la oportunidad de que lo impregnen con su cultura.


Esto, contenido por los **conjuntos de viviendas, capaces de amortiguar el confort interior y el clima exterior, habitando un manto que como un ágora es capaz de abrazar las interacciones sociales**. Un hogar con un espacio intermedio que sirve de transición y que cobija la vida comunitaria que hemos perdido, un hogar de madera que refresca en verano y me guarece en invierno.



Net Zero Energía

Según el Ministerio de energía "El sector de la edificación es responsable del 23% del consumo de energía final y representa el 7% del total de emisiones de CO2 en Chile".

Se propone el reducir la demanda energética de las viviendas mediante una envolvente térmica de alto desempeño con el objetivo de minimizar los esfuerzos de generación energética, y con ello disminuir los gastos de mantención asociados, considerando que es una vivienda social.

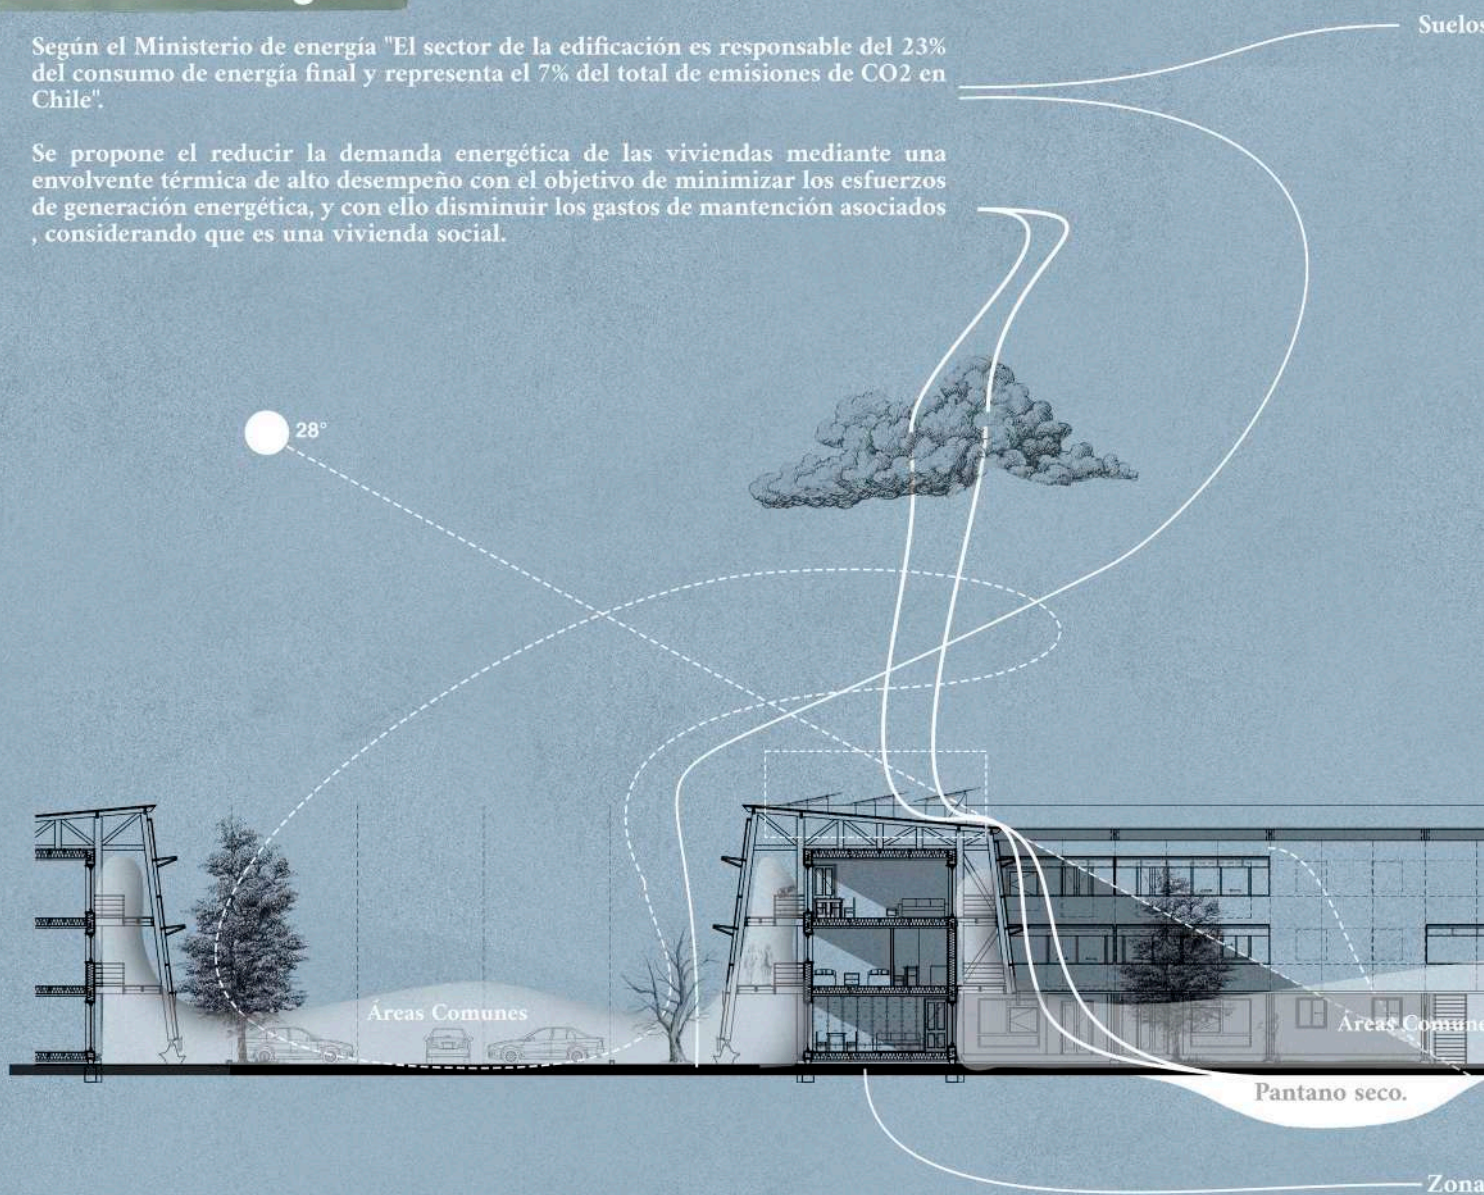

Economía Circular

Se plantean casas con tabiques ligeros para flexibilizar el espacio y las adaptaciones que cada familia requiera. Por otro lado, se consideran aislantes fabricados con materiales reciclados provenientes de industrias cercanas. Además, se incorporan mecanismos de reciclaje de aguas grises a través de pantanos secos para utilizar en procesos de cultivo con compostaje de residuos orgánicos en huertos comunitarios.

Además, se utilizará un sistema de recolección de aguas lluvias, que se empleará en el riego para reducir la demanda de agua en el espacio público.

s naturales.


edificada.



Industrialización

Industrialización

Industrialización

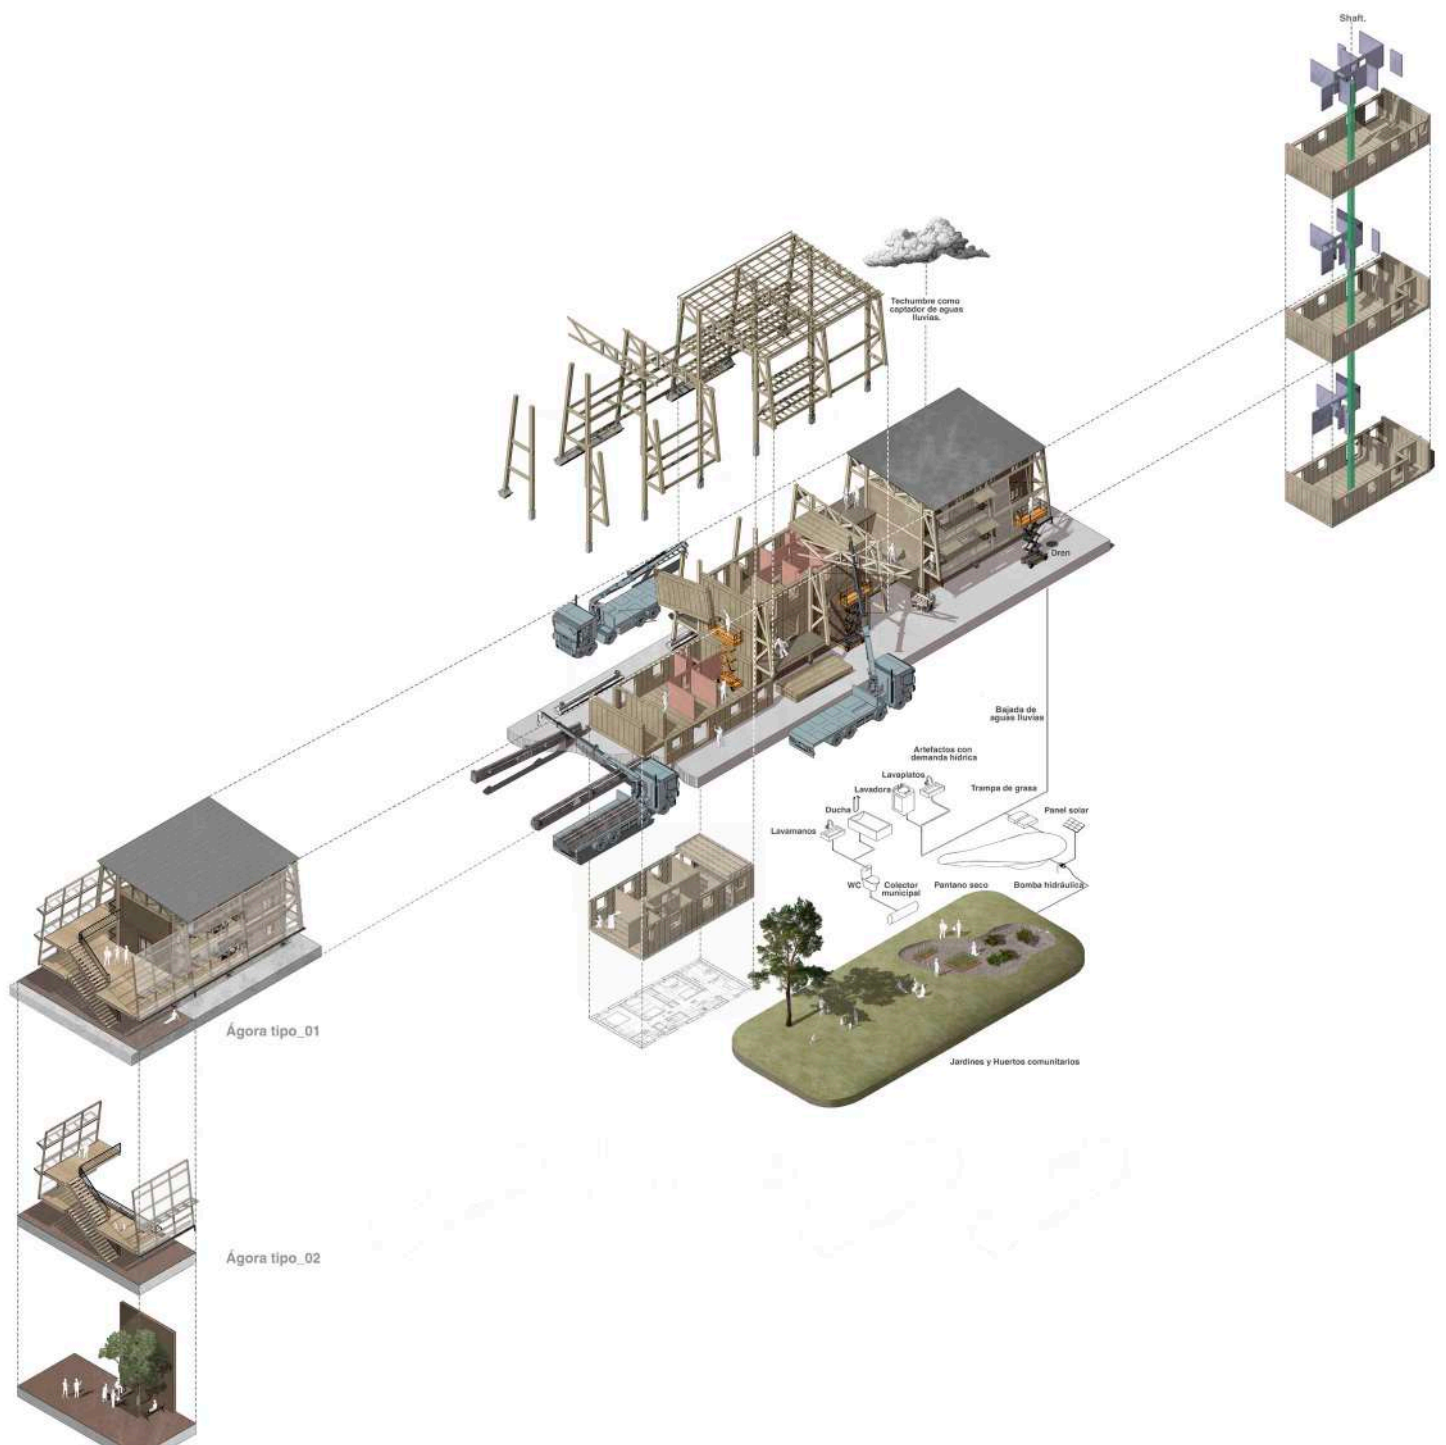


Conformación del Ágora

Las viviendas requerían una junta de dilatación cada ciertos tramos. A partir de eso, surge la idea de que estas juntas se expandan, **generando también un espacio techado donde puedan desarrollarse actividades sociales** durante el invierno, ya sea a nivel de suelo o en los pisos superiores del edificio, permitiendo así **variadas configuraciones para el encuentro entre vecinos**.








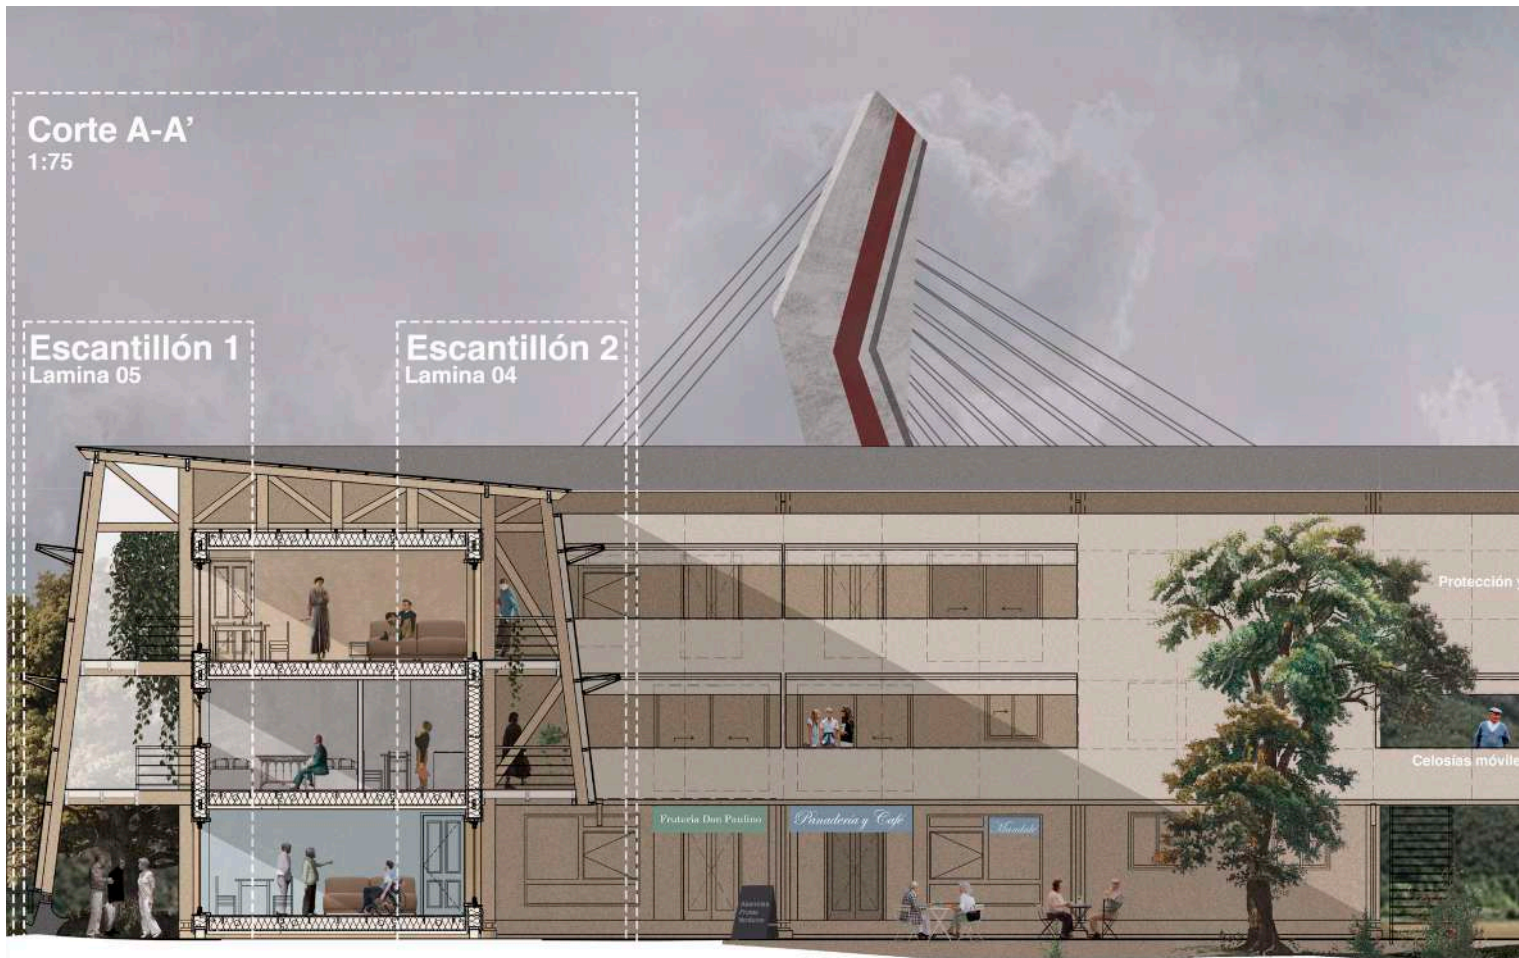


Elevación frontal.
1:75

Corte B-B'
1:75

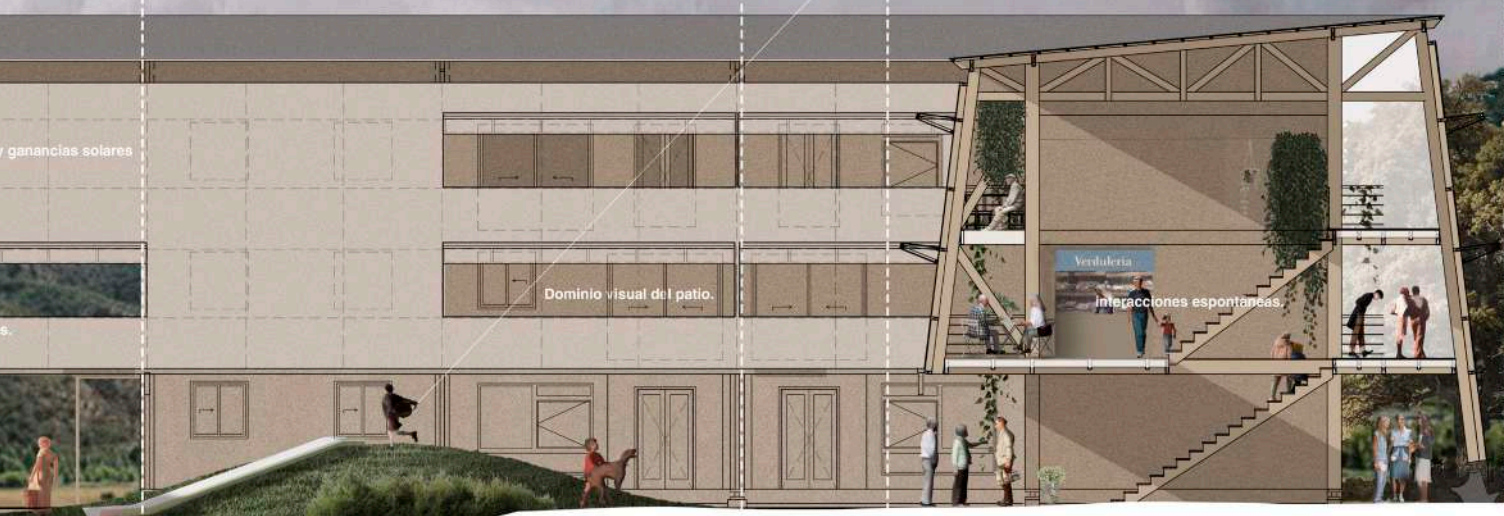

...la cohesión social.

Elevación posterior.
1:75

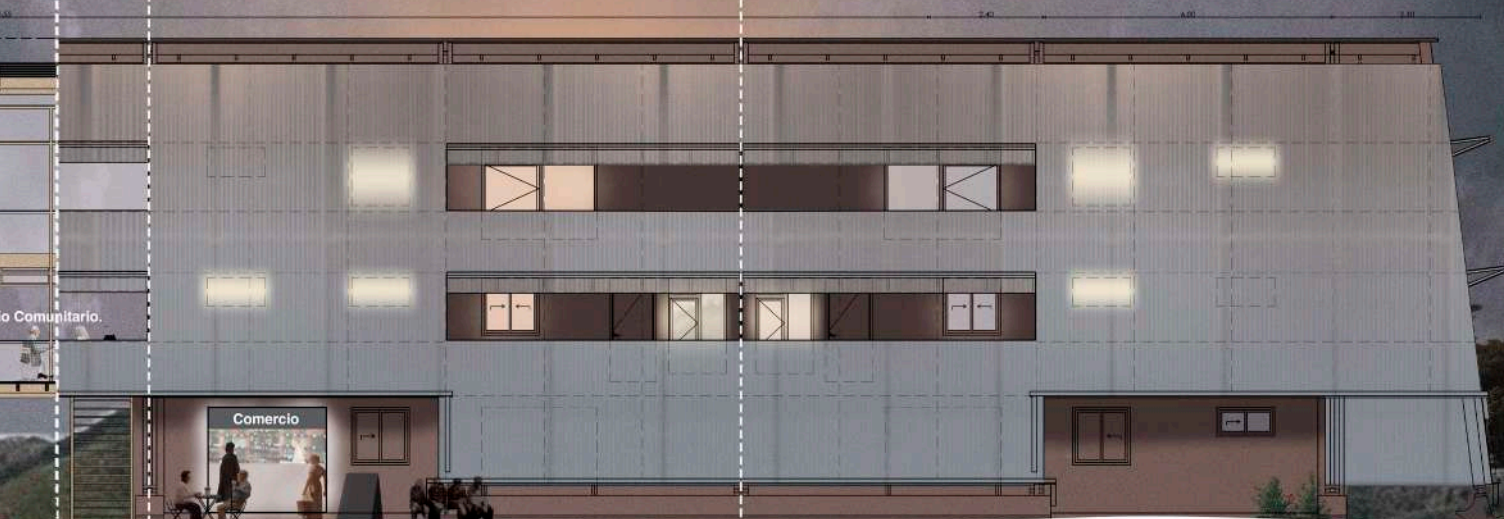

Gracias por ver.